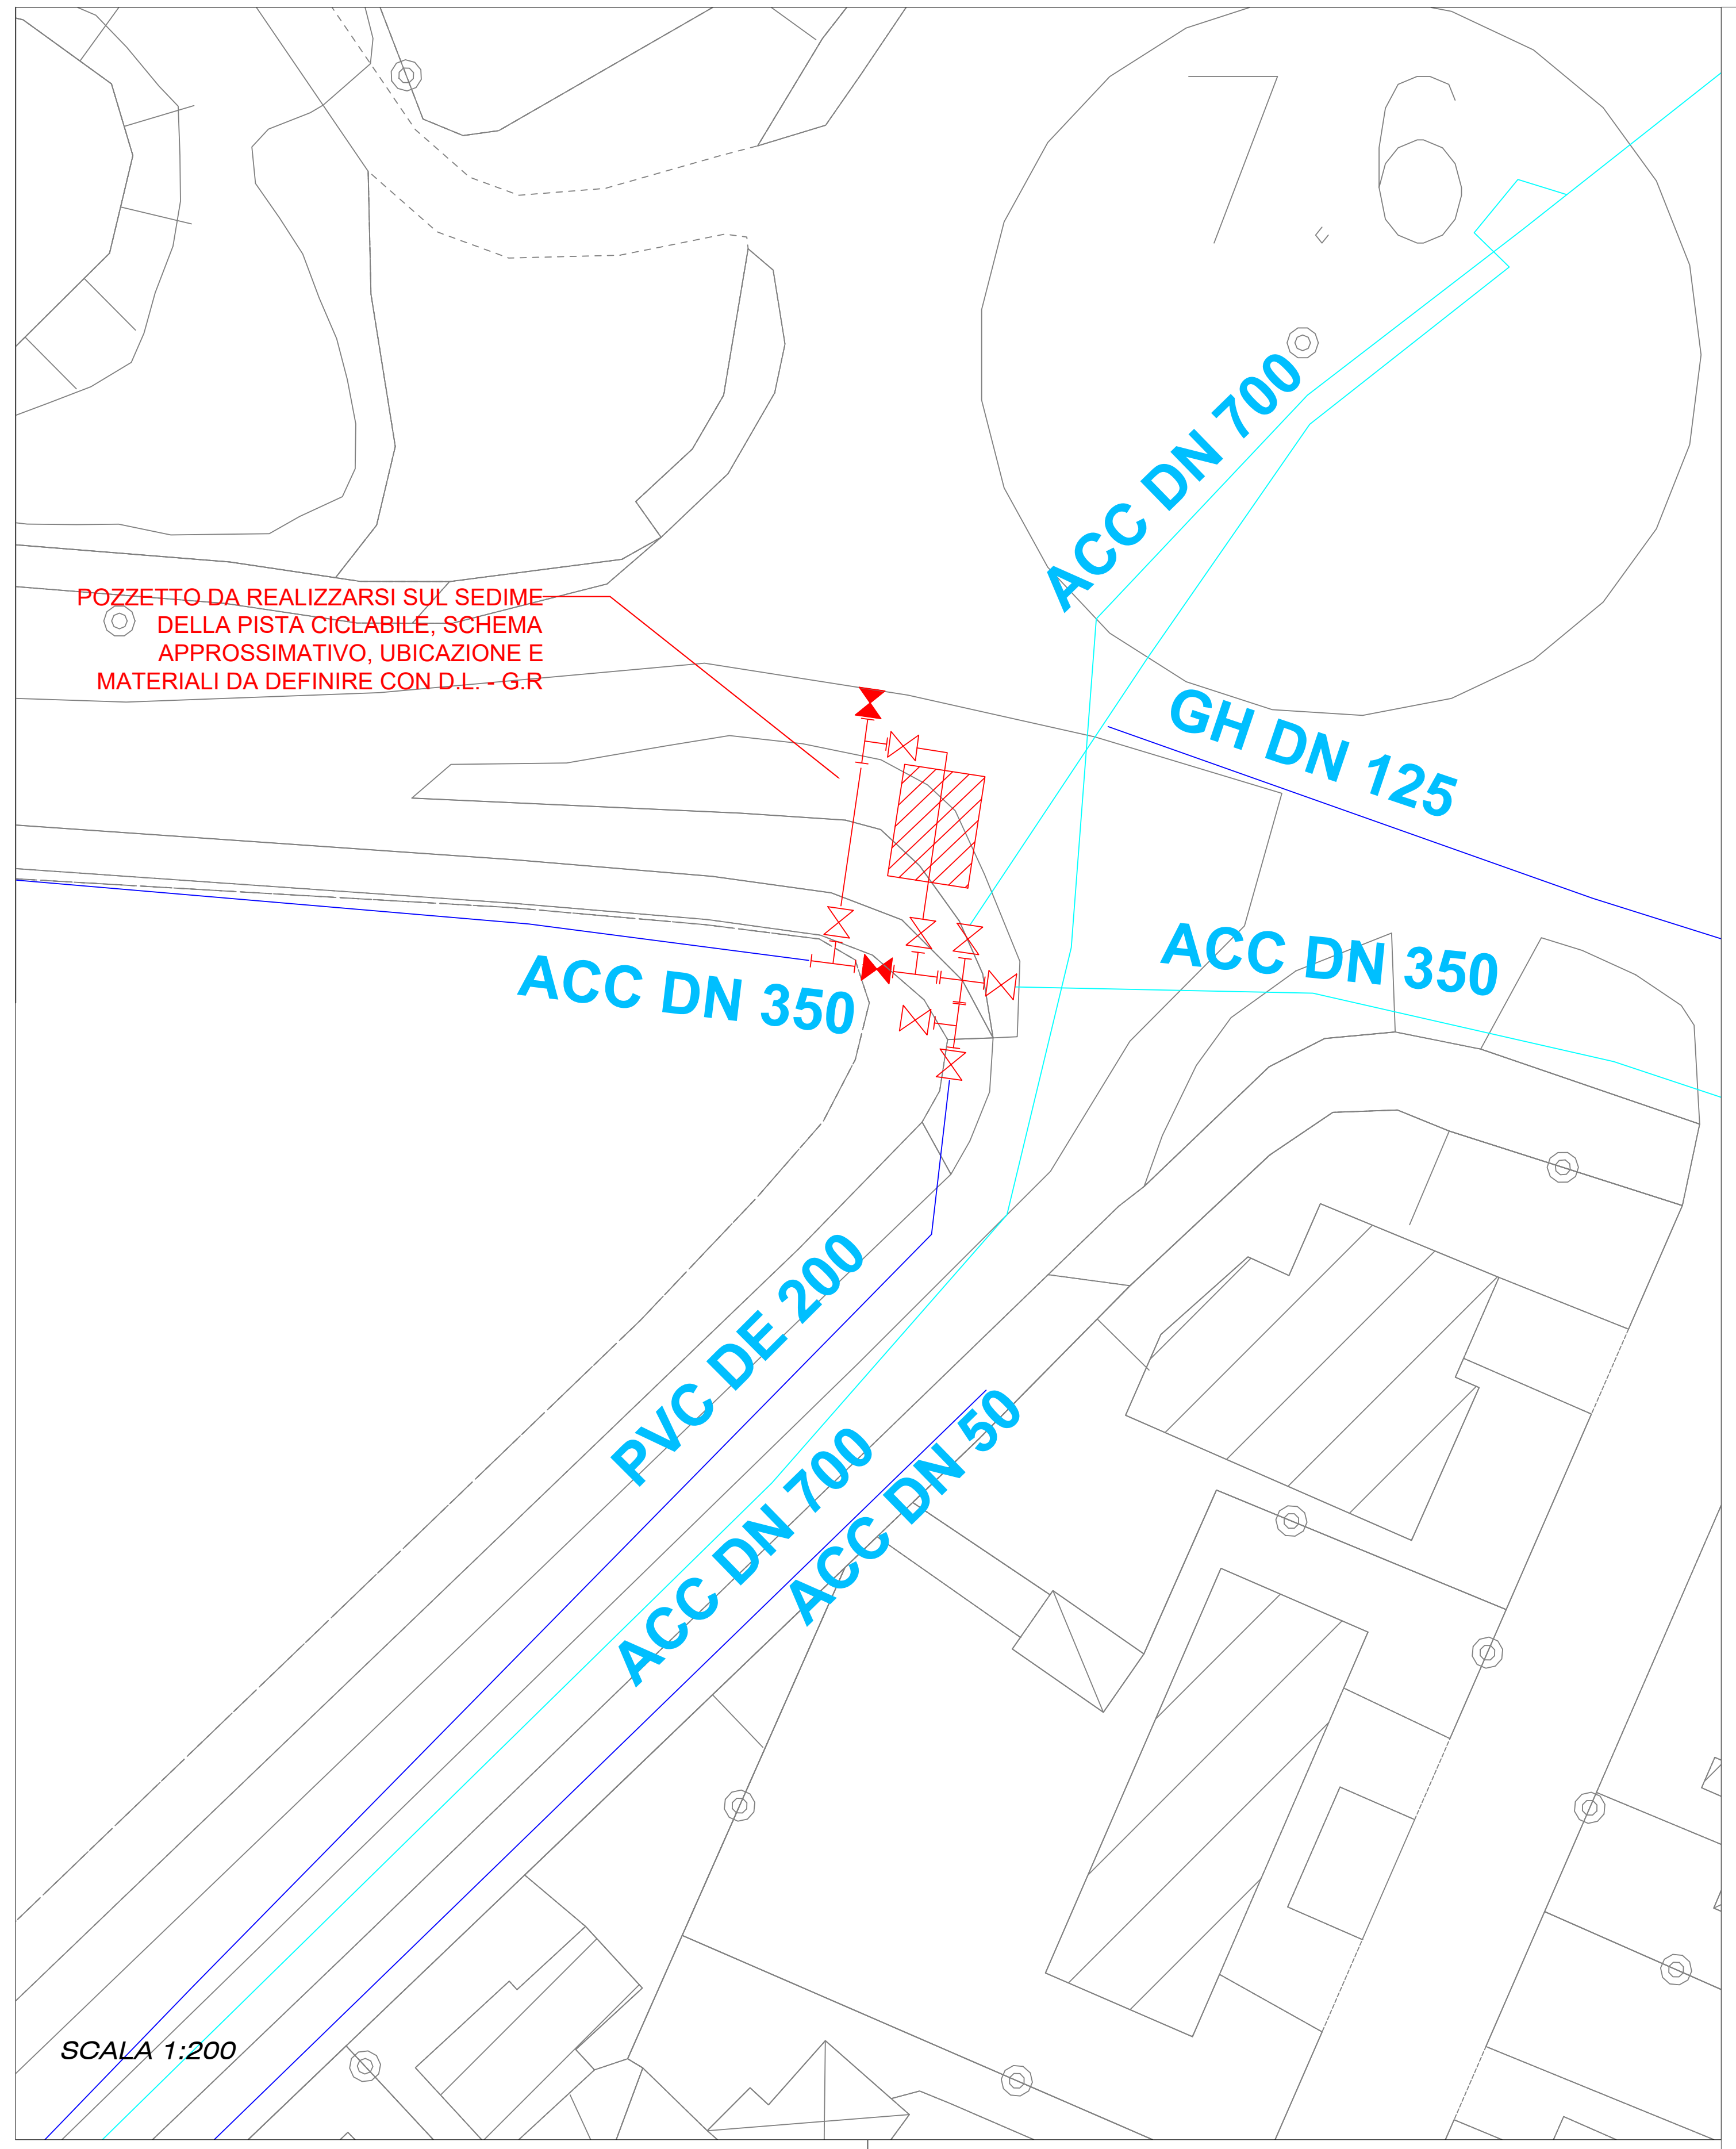
POZZETTO DA REALIZZARSI SUL SEDIME DELLA PISTA CICLABILE, SCHEMA APPROSSIMATIVO, UBICAZIONE E MATERIALI DA DEFINIRE CON D.L. - G.R
ACC DN 700
GH DN 125
ACC DN 350
ACC DN 350
PVC DE 200
ACC DN 700
ACC DN 50
7.6

SCALA 1:200

etra

A1939 Particolare pozzetto nuovo misuratore per
la rete idrica nel Comune di Galzignano Terme

Particolare pozzetto nodo idraulico
Ubicazione e ricollegamenti da definire con G.R.
TAV 1

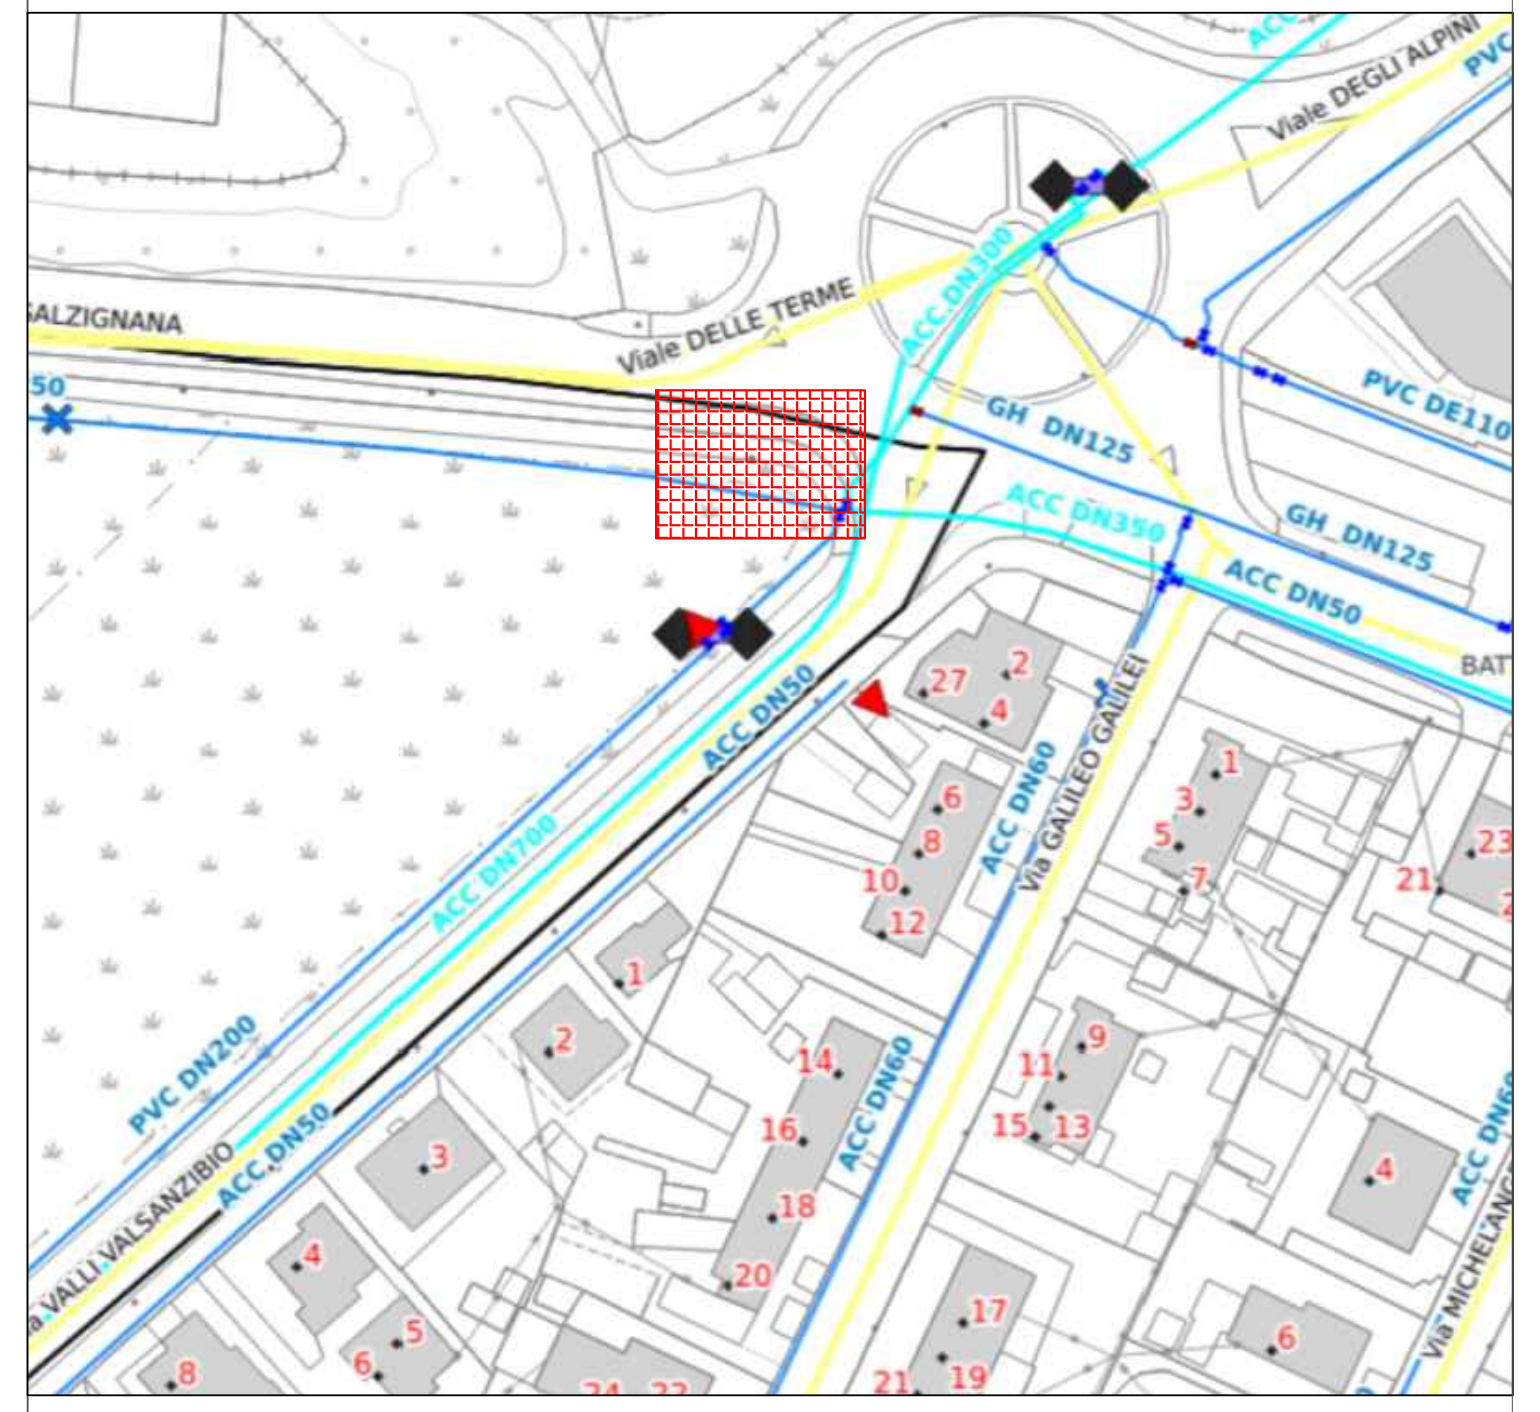

▦ AREA DI INTERVENTO

REVISIONE: 00			
ESEGUITO da: Ing. Francesco Munari			
CAPO COMMESSA: Ing.Loris Pavanetto	Data	codice ATO	FILE dwg
CONTROLLATO Responsabile PRO:	Novembre 2025		
APPROVATO Responsabile ING:			

ETRA S.p.A.
Largo Parolini, 82/b - 36061 Bassano del Grappa (VI) - tel. 049 8098000 fax 049 8098001
Internet: www.etraspa.it e-mail: info@etraspa.it

ETRA S.p.A. si riserva la proprieta' del disegno, vietandone la riproduzione e la divulgazione senza autorizzazione a' sensi delle vigenti leggi

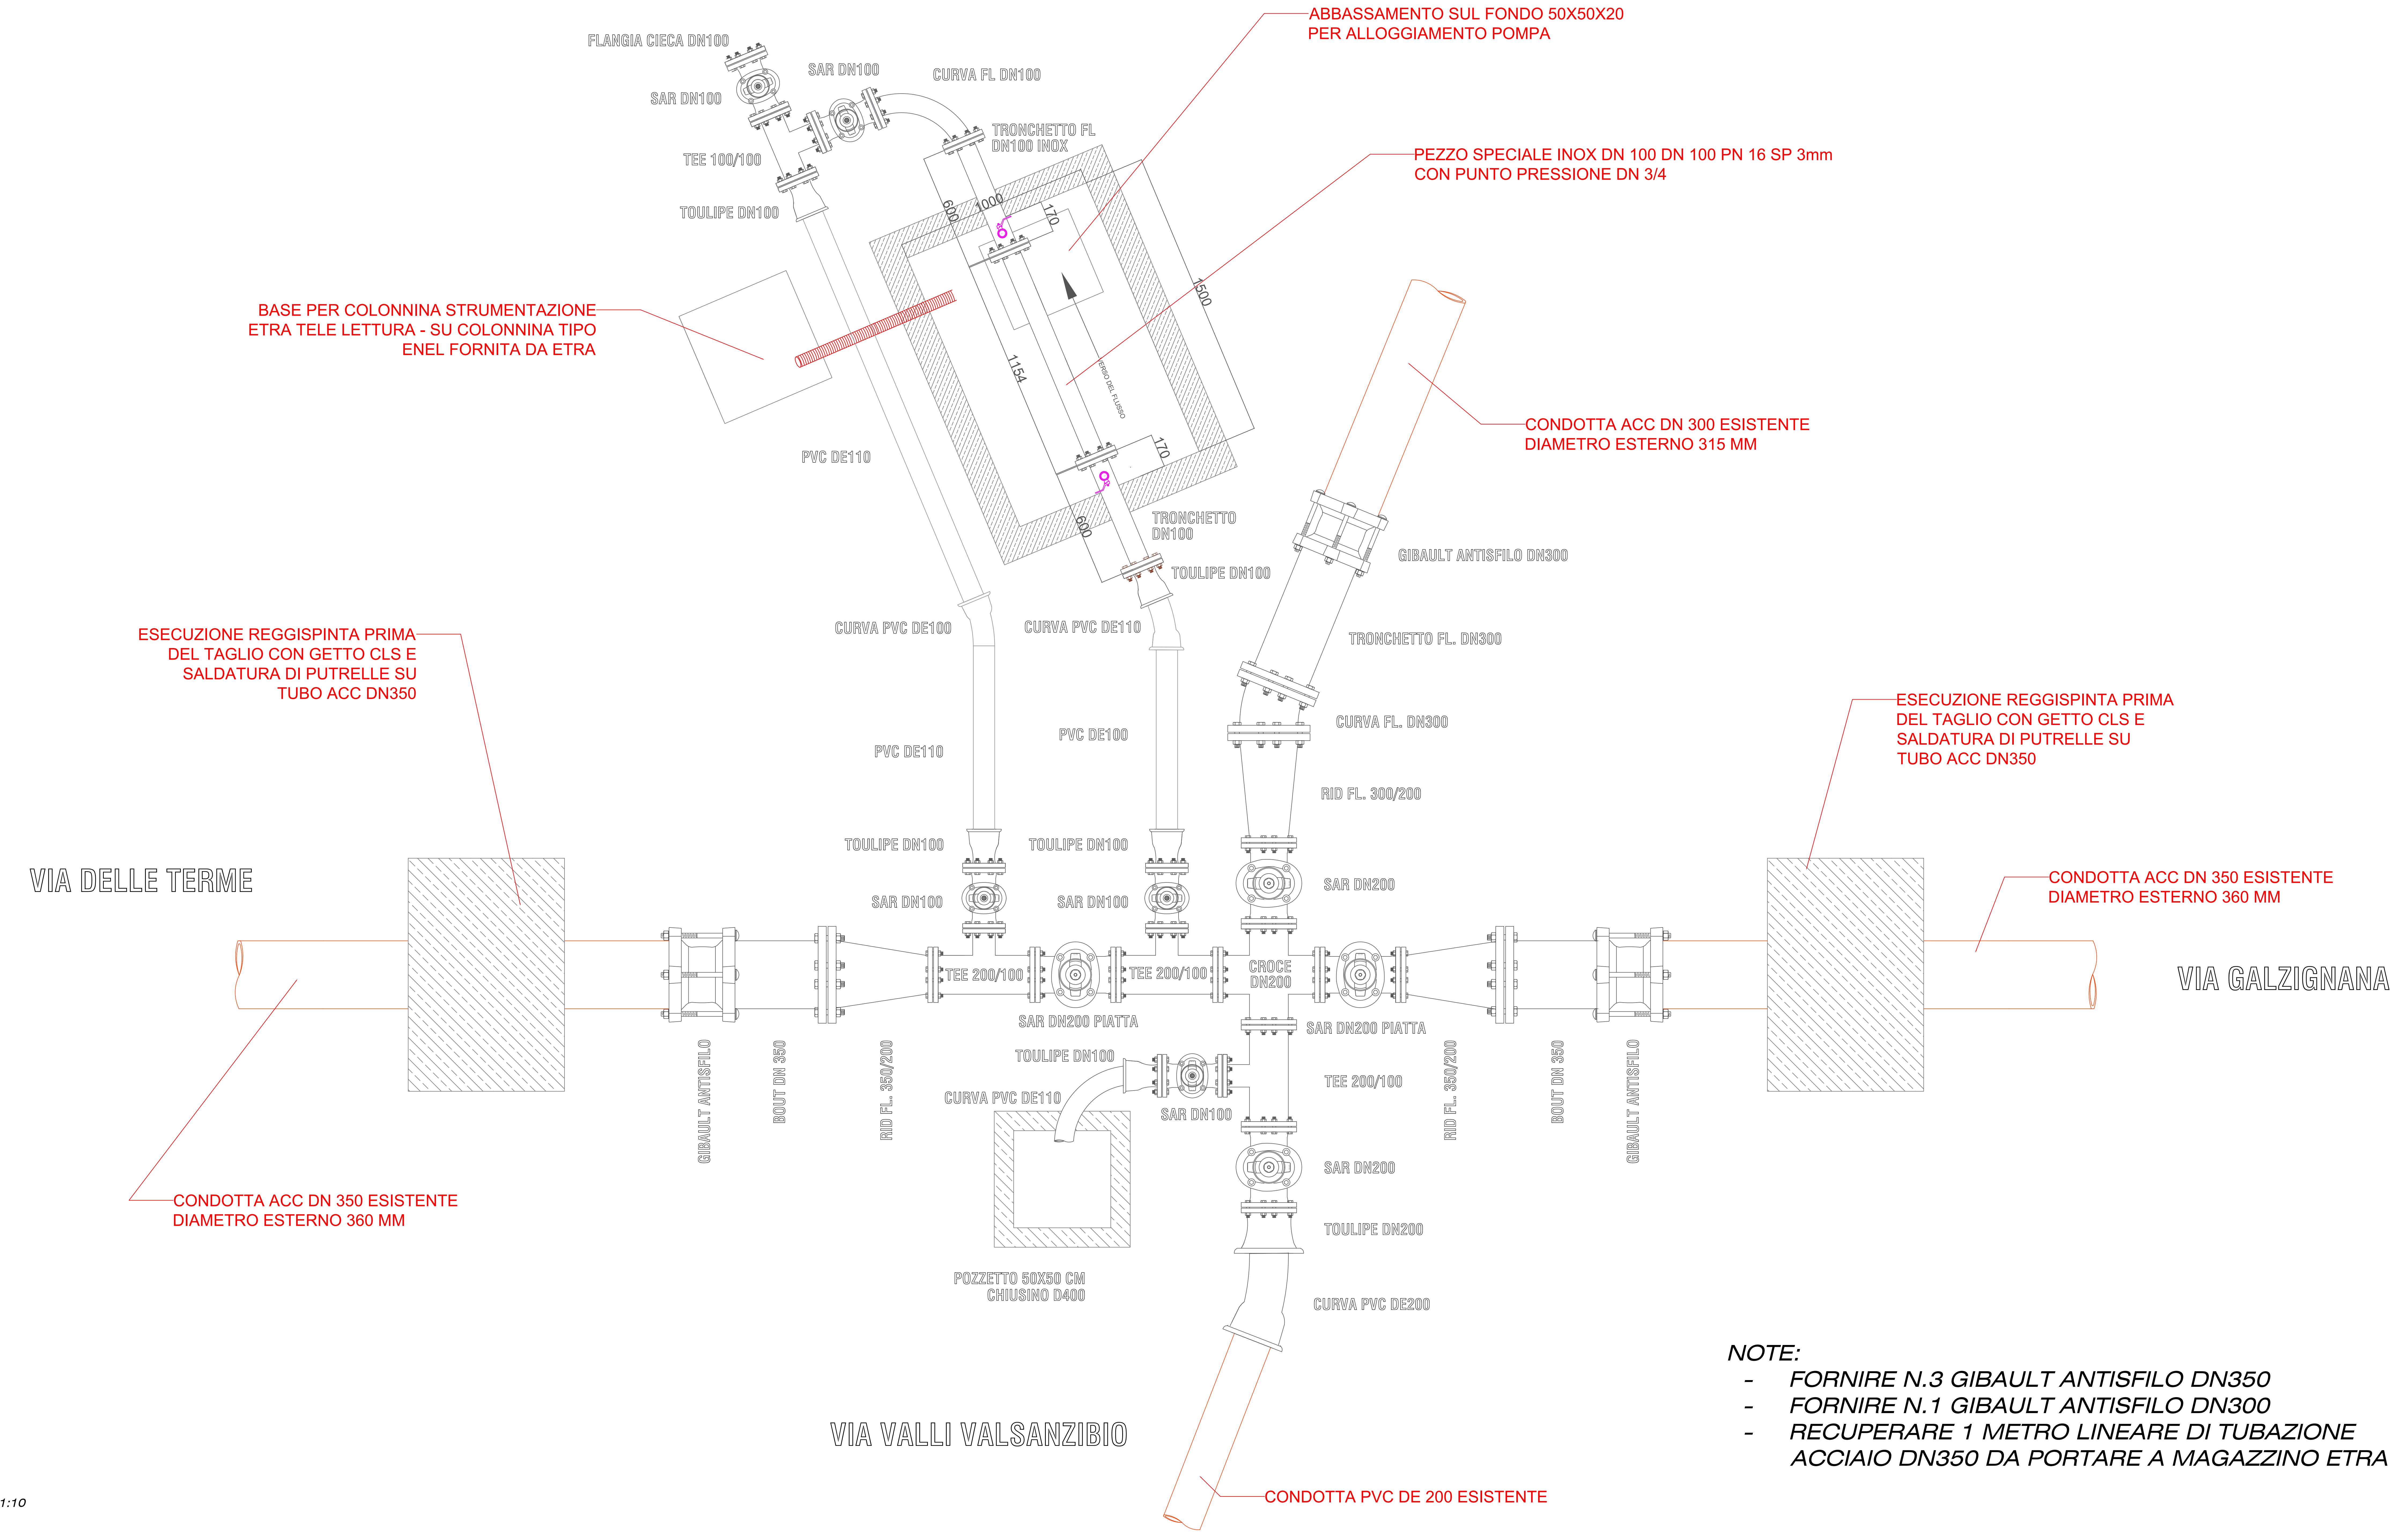

SCALA 1:10

NOTE:
- *FORNIRE N.3 GIBAULT ANTISFILO DN350*
- *FORNIRE N.1 GIBAULT ANTISFILO DN300*
- *RECUPERARE 1 METRO LINEARE DI TUBAZIONE ACCIAIO DN350 DA PORTARE A MAGAZZINO ETRA*